

VILLA DE MAÎTRE SIS A HAMMAMET

DOSSIER D'EXECUTION

BASSATINE II

MAITRE D'OUVRAGE: **FAMILLE MR ET MME
MONIA GUEZIH**

MAITRE D'OEUVRE: **LEADERS BUILDING**



EN FACE CLINIQUE HANNIBAL , LES BERGES DU LAC 2



[HTTPS://LEADERS-BUILDING.COM](https://leaders-building.com)



LEADERS®
BUILDING



+216 27 246 339



LEADERSBUILDING@GMAIL.COM



PROJET

VILLA SISE À
HAMMAMET

PLAN MACONNERIE
RDC

MAITRE
D'OUVRAGE

MME GHEZIH
MONIA

ECHELLE

DATE



PAGE

CONTACT

TEL: +216 27 246 345

E.MAIL

CONTACT.TUNISIE@LEADERS-BUILDING.COM

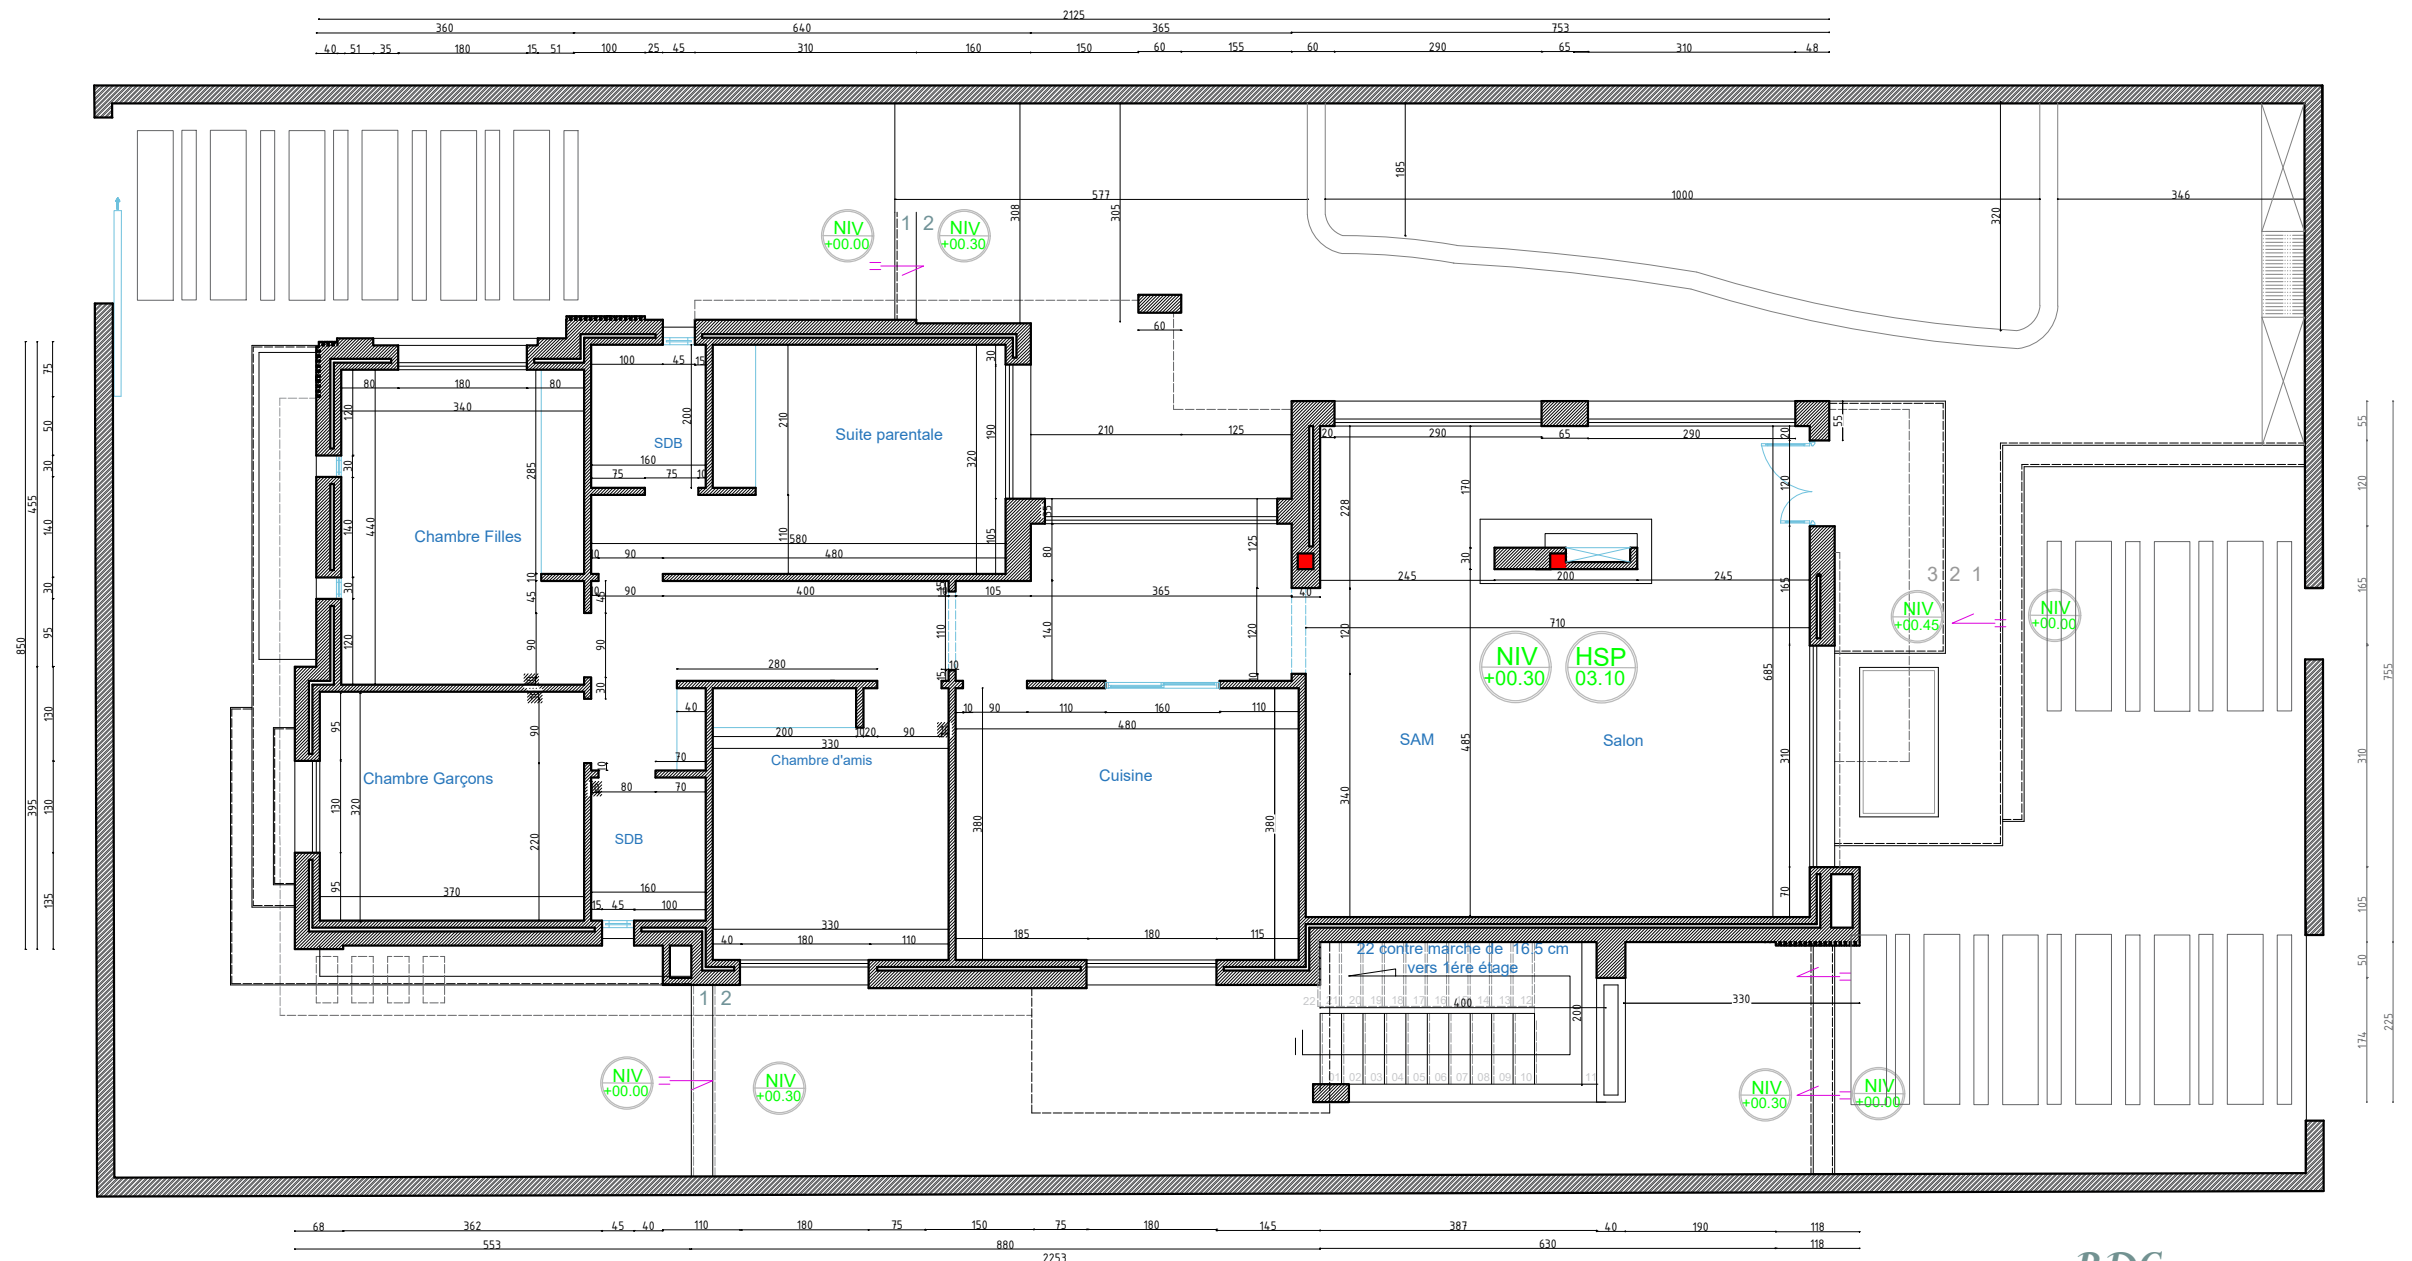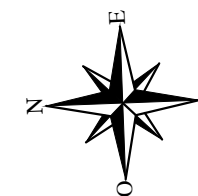

RDC



PROJET

VILLA SISE À
HAMMAMET

PLAN MACONNERIE
ETAGE

MAITRE
D'OUVRAGE

MME GHEZIH
MONIA

ECHELLE

DATE





PAGE

CONTACT


TEL: +216 27 246 345

E.MAIL


CONTACT.TUNISIE@LEADERS-BUILDING.COM

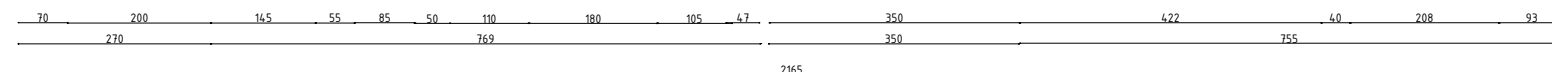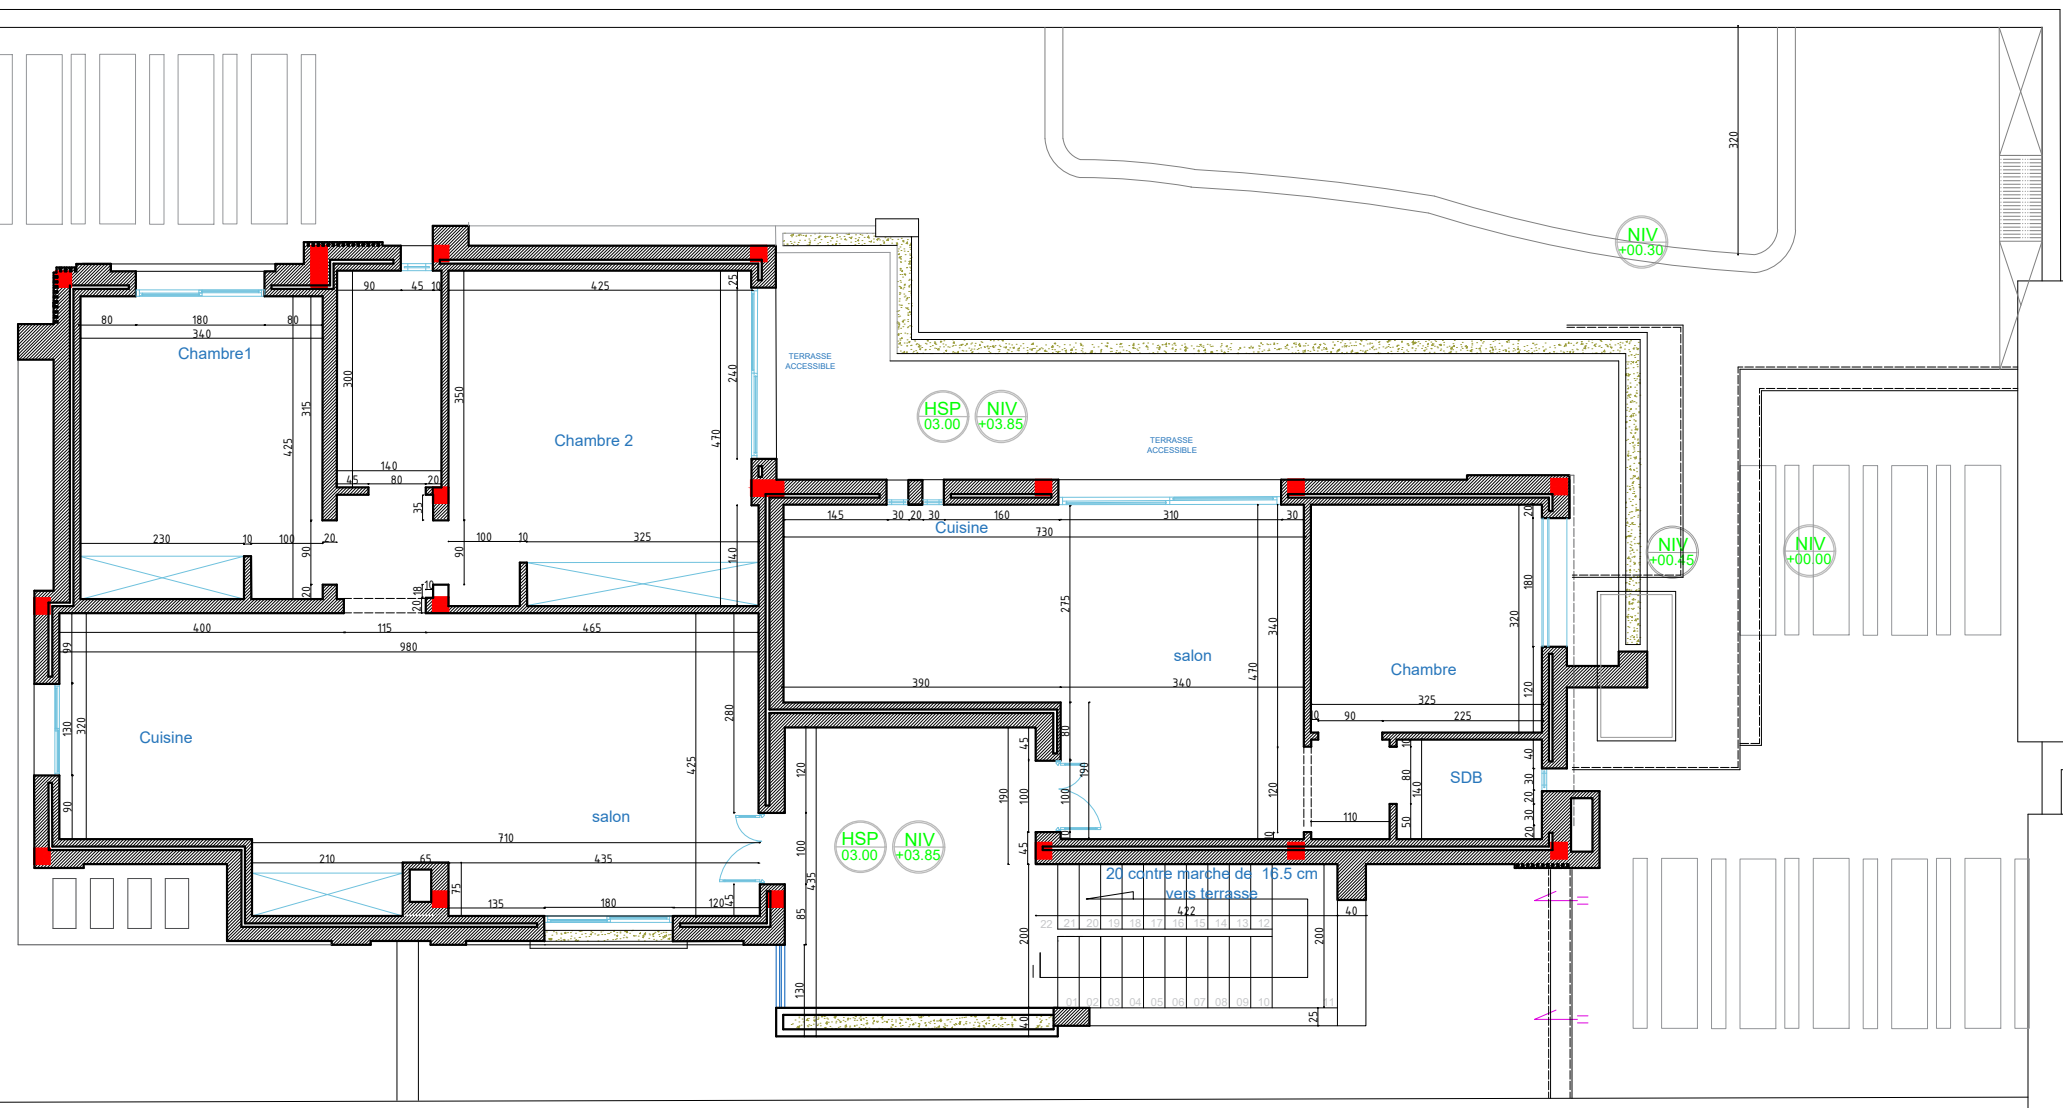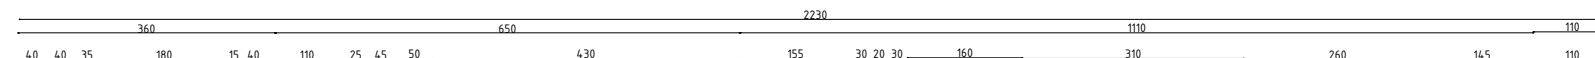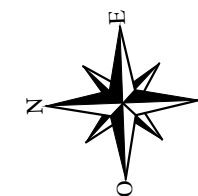

ETAGE

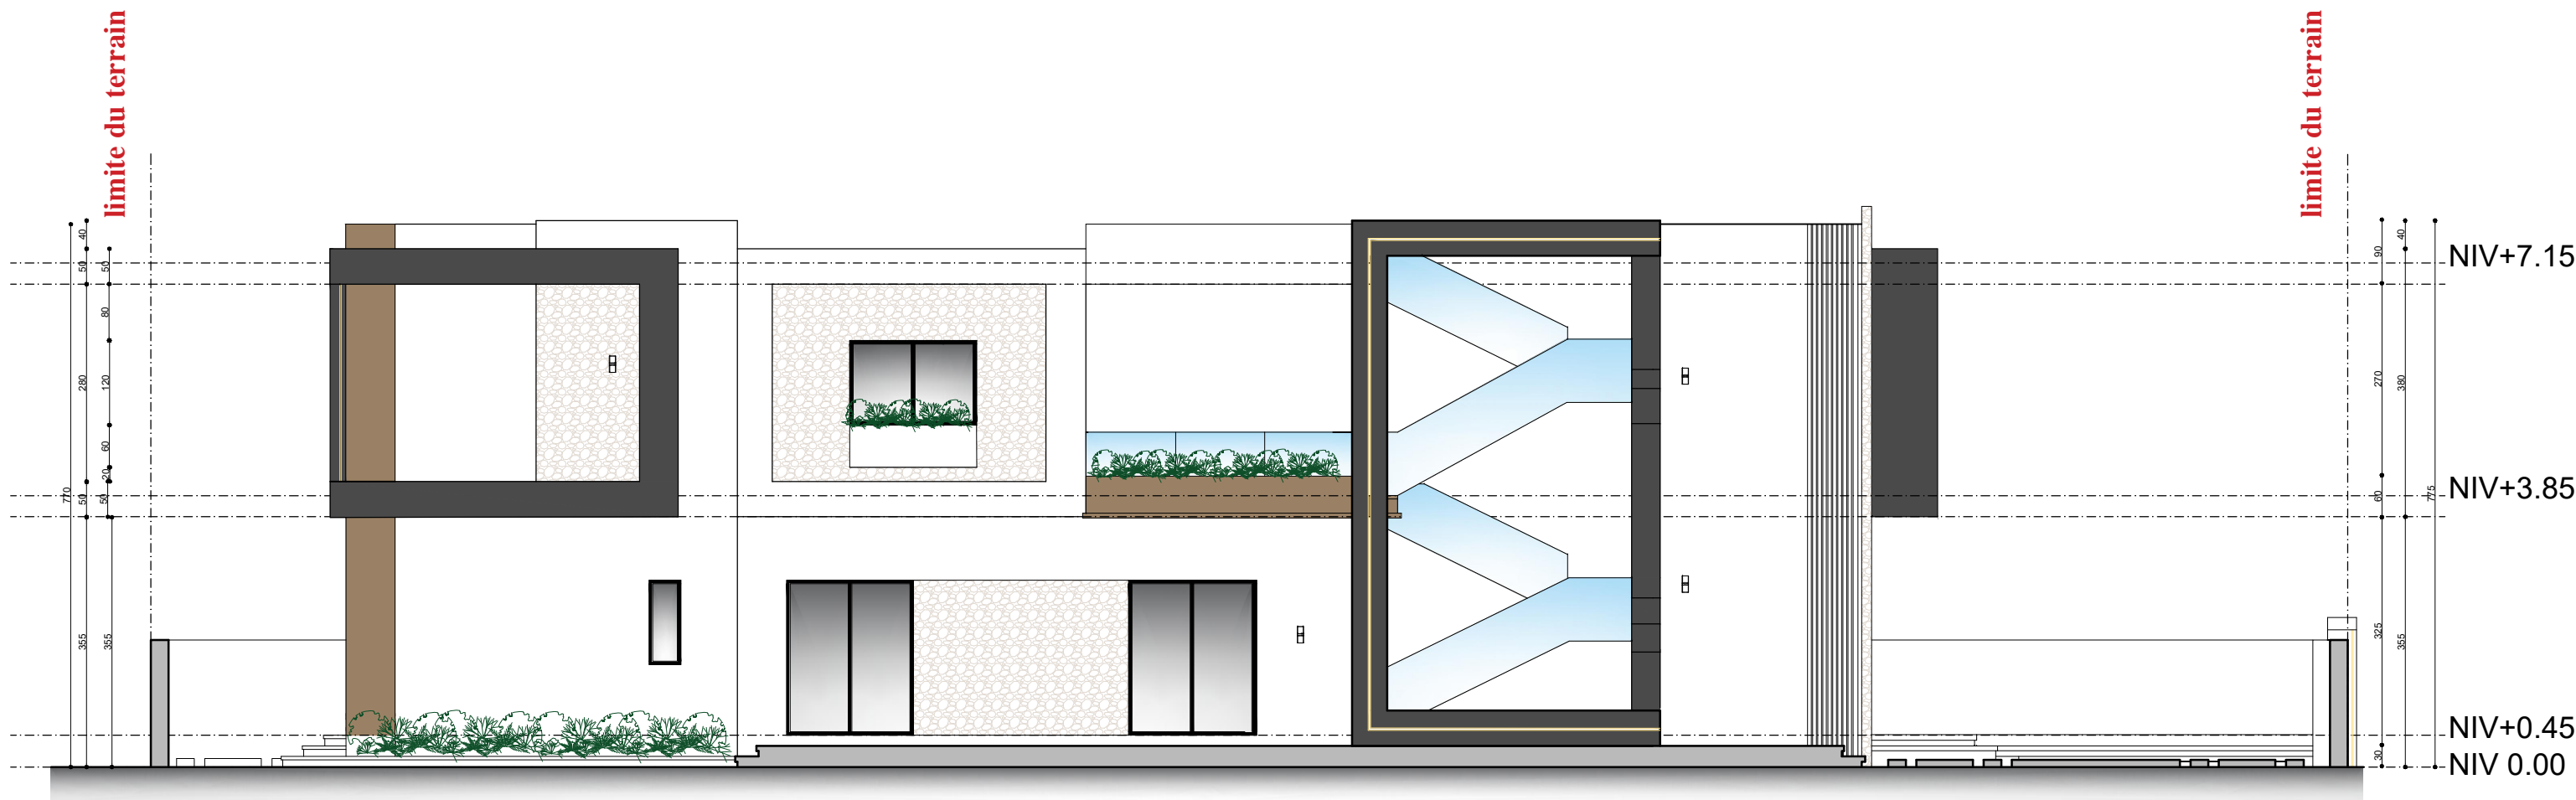

FAÇADE OUEST

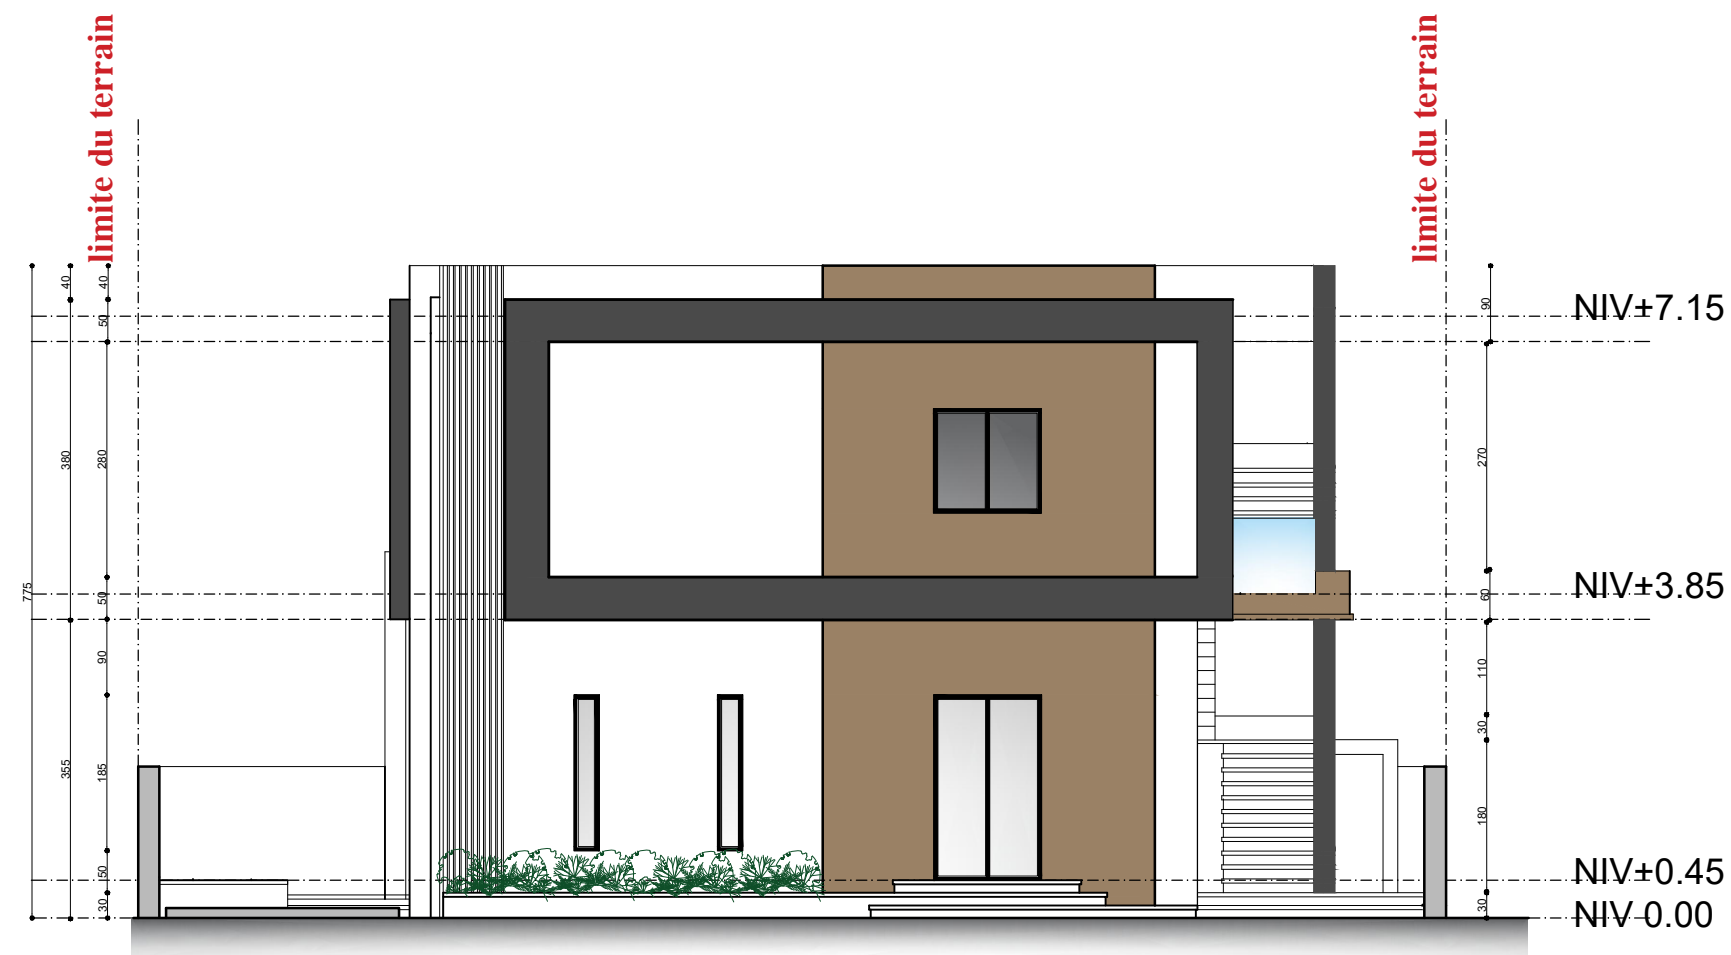

FAÇADE NORD

